


Contractor As Drawn

7 storeys, 528 m² on a 3.96 × 25.00 m plot

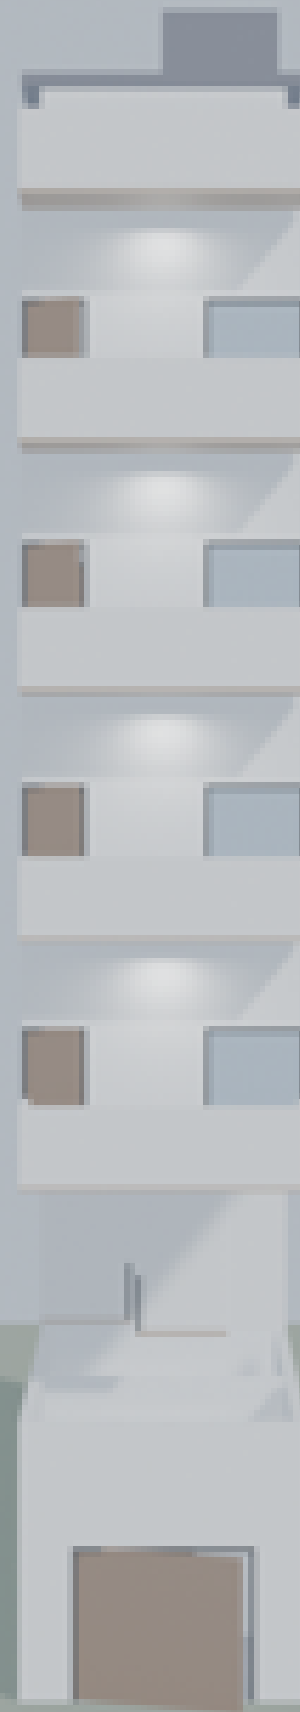

Design Intent

A seven-storey Vietnamese tube house (trệt / lầu / tầng 2–5 / sân thượng) reconstructed from the contractor's own drawing set on a 3,960 × 25,000 mm plot, with the drawn core — a 3,005 mm U-return stair, a 1,500 × 1,600 lift and a light well — repeated identically on every level.

The ground floor runs garage → living room (P.KHÁCH) → stair core → WC → combined kitchen + dining (BẾP & ĂN); the mezzanine opens a double-height void over the garage and living room (declared as a storey void, not a fake room) with the family room (P.SINH HOẠT) at the rear; floors 2–4 repeat two bedrooms (one front with ensuite and balcony, one rear); floor 5 carries the altar room (P.THỜ); the roof terrace (SÂN THƯỢNG) opens front and rear with the lift plant room (Ồ KỸ THUẬT THANG MÁY) standing on the roof slab.

All departures from the drawing are ledgered in designs/contractor-as-drawn.fidelity.md: the stair shaft is enlarged to 3,005 × 4,000 mm to hold a Blondel-compliant U-return, the lift shaft is inferred (no shaft is labelled on the floor plans), and the roof glazing is represented by an open roof void over the stair rather than glass.

Room Schedule


Floor	Room	Type	Area (m²)
Ground	gara	garage	15.8
Ground	khach	living	19.0
Ground	stairwell	stairwell	12.0
Ground	hall_stair	hall	3.8
Ground	elevator	elevator	3.6
Ground	hall_elev	hall	3.5
Ground	wc_gf	wc	6.3
Ground	bep_an	kitchen	16.2
Mezzanine	stairwell	stairwell	12.0
Mezzanine	hall_stair	hall	3.8
Mezzanine	elevator	elevator	3.6
Mezzanine	hall_elev	hall	3.5
Mezzanine	sinh_hoat	living	22.6
Floor 2	ban_cong_f2	balcony	5.5
Floor 2	ngu_truoc_f2	bedroom	15.8
Floor 2	wc_truoc_f2	wc	3.1
Floor 2	hall_wc_f2	hall	3.2
Floor 2	hall_front_f2	hall	7.1
Floor 2	stairwell	stairwell	12.0
Floor 2	hall_stair	hall	3.8
Floor 2	elevator	elevator	3.6
Floor 2	hall_elev	hall	3.5
Floor 2	wc_sau_f2	wc	6.3
Floor 2	ngu_sau_f2	bedroom	16.2
Floor 3	ban_cong_f3	balcony	5.5
Floor 3	ngu_truoc_f3	bedroom	15.8
Floor 3	wc_truoc_f3	wc	3.1
Floor 3	hall_wc_f3	hall	3.2
Floor 3	hall_front_f3	hall	7.1
Floor 3	stairwell	stairwell	12.0
Floor 3	hall_stair	hall	3.8

Floor	Room	Type	Area (m²)
Floor 3	elevator	elevator	3.6
Floor 3	hall_elev	hall	3.5
Floor 3	wc_sau_f3	wc	6.3
Floor 3	ngu_sau_f3	bedroom	16.2
Floor 4	ban_cong_f4	balcony	5.5
Floor 4	ngu_truoc_f4	bedroom	15.8
Floor 4	wc_truoc_f4	wc	3.1
Floor 4	hall_wc_f4	hall	3.2
Floor 4	hall_front_f4	hall	7.1
Floor 4	stairwell	stairwell	12.0
Floor 4	hall_stair	hall	3.8
Floor 4	elevator	elevator	3.6
Floor 4	hall_elev	hall	3.5
Floor 4	wc_sau_f4	wc	6.3
Floor 4	ngu_sau_f4	bedroom	16.2
Floor 5	ban_cong_f5	balcony	5.5
Floor 5	tho_f5	living	15.8
Floor 5	hall_front_f5	hall	13.5
Floor 5	stairwell	stairwell	12.0
Floor 5	hall_stair	hall	3.8
Floor 5	elevator	elevator	3.6
Floor 5	hall_elev	hall	3.5
Floor 5	wc_sau_f5	wc	6.3
Floor 5	ngu_sau_f5	bedroom	16.2
Roof Terrace	san_thuong_truoc	terrace	34.8
Roof Terrace	stairwell	stairwell	12.0
Roof Terrace	hall_stair	hall	3.8
Roof Terrace	elevator	elevator	3.6
Roof Terrace	hall_elev	hall	3.5
Roof Terrace	san_thuong_sau	terrace	22.6


Floor Totals

Ground	80.2 m²
Mezzanine	45.5 m²
Floor 2	80.1 m²
Floor 3	80.1 m²
Floor 4	80.1 m²
Floor 5	80.2 m²
Roof Terrace	80.3 m²


Ground — Floor Plan

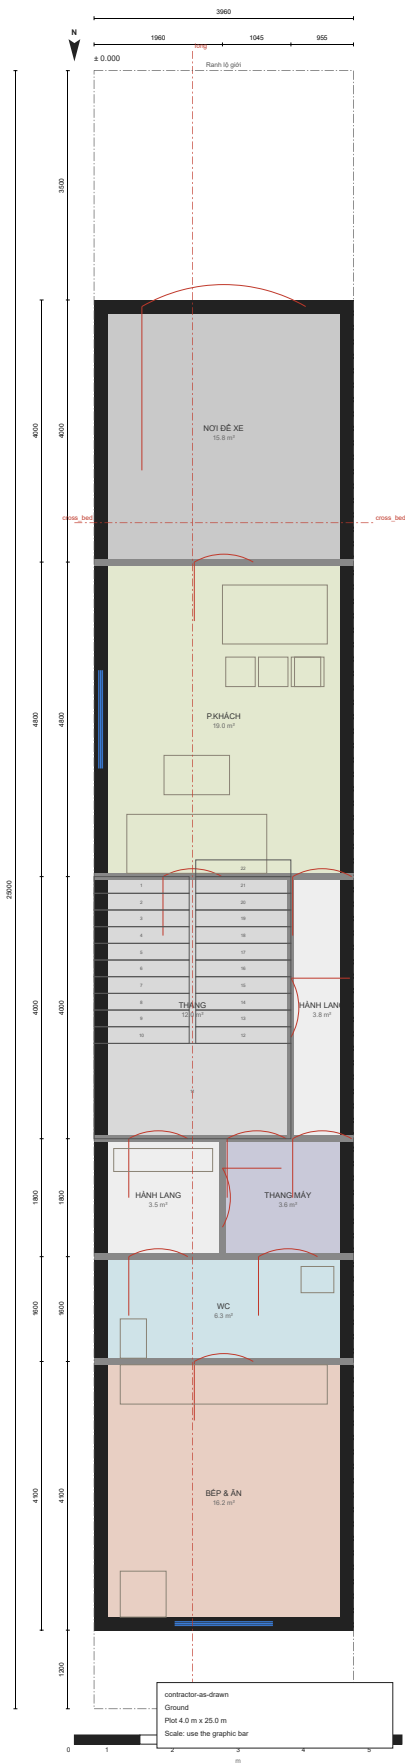


Mezzanine — Floor Plan

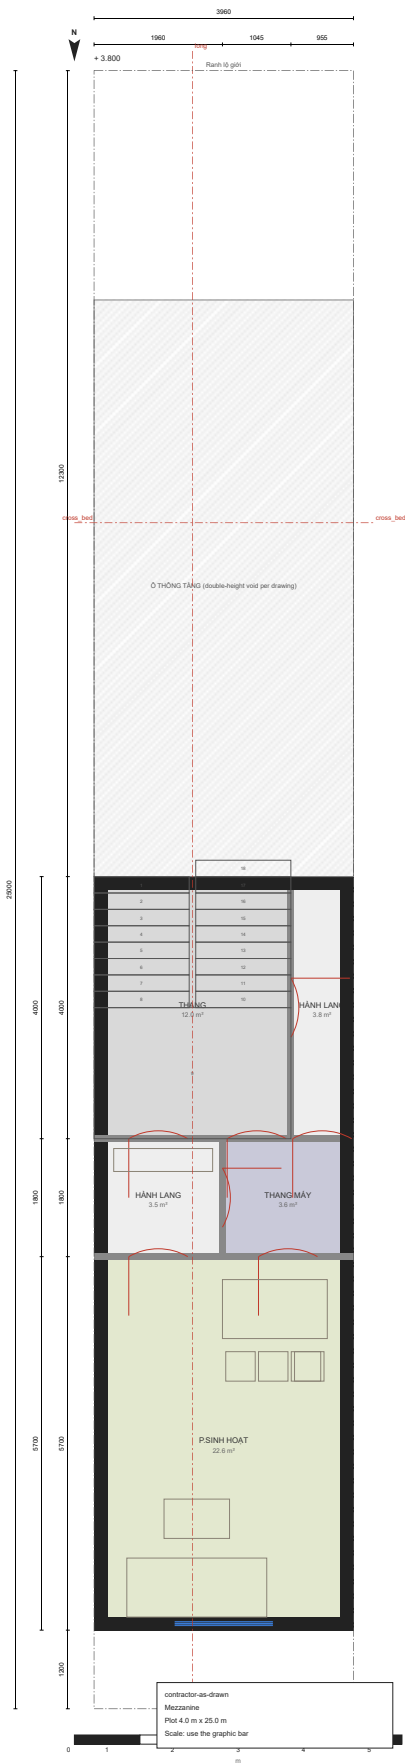


Floor 2 — Floor Plan

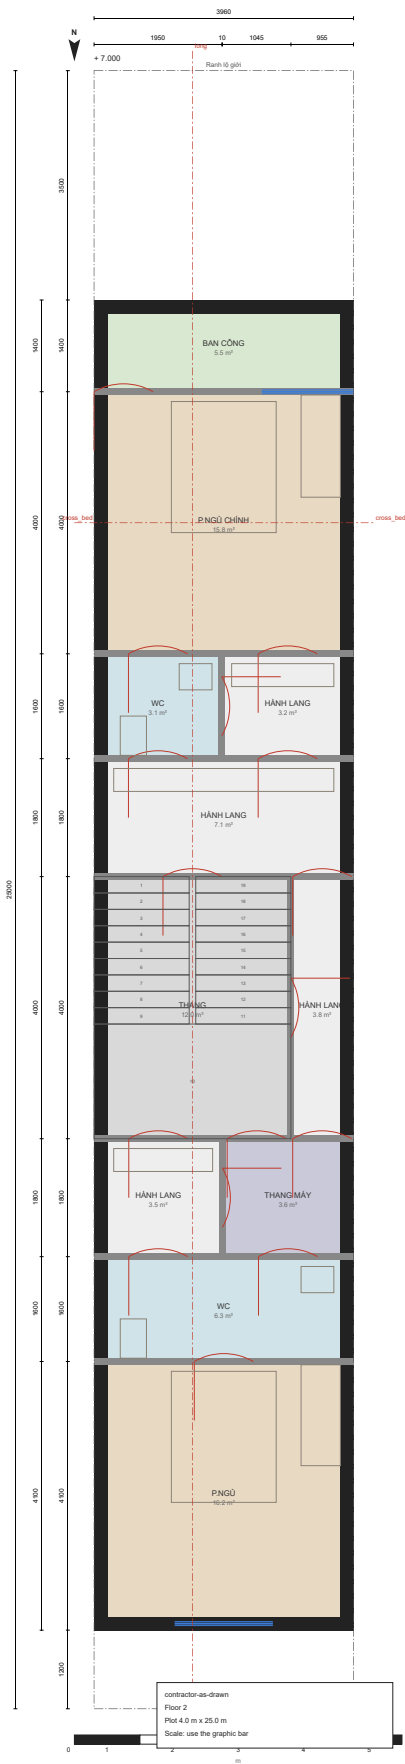


Floor 3 — Floor Plan

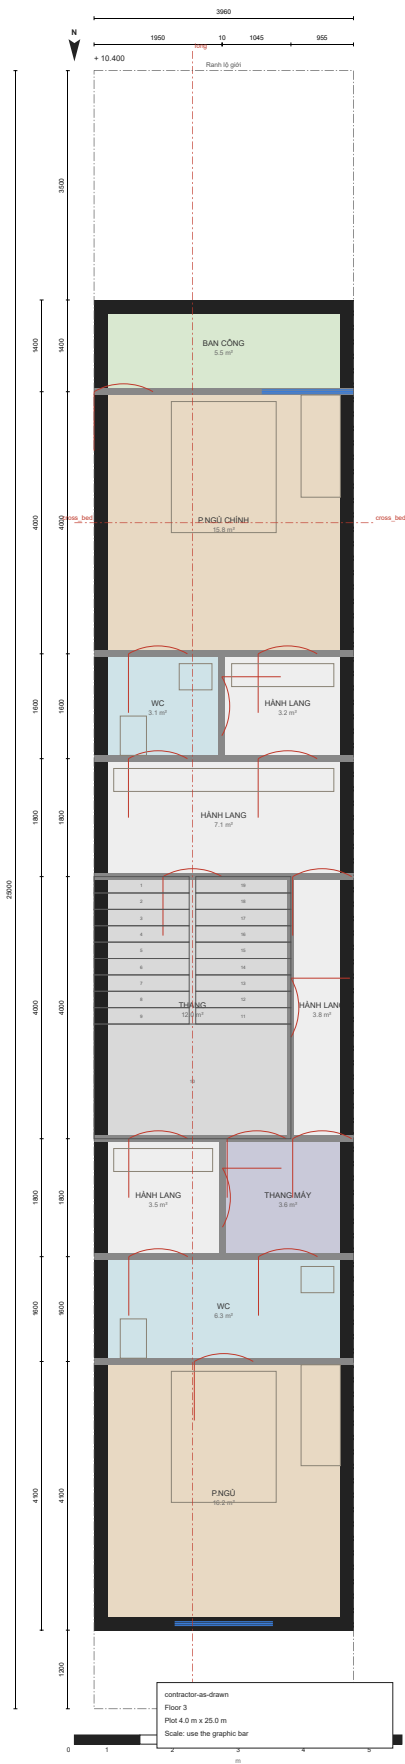


Floor 4 — Floor Plan

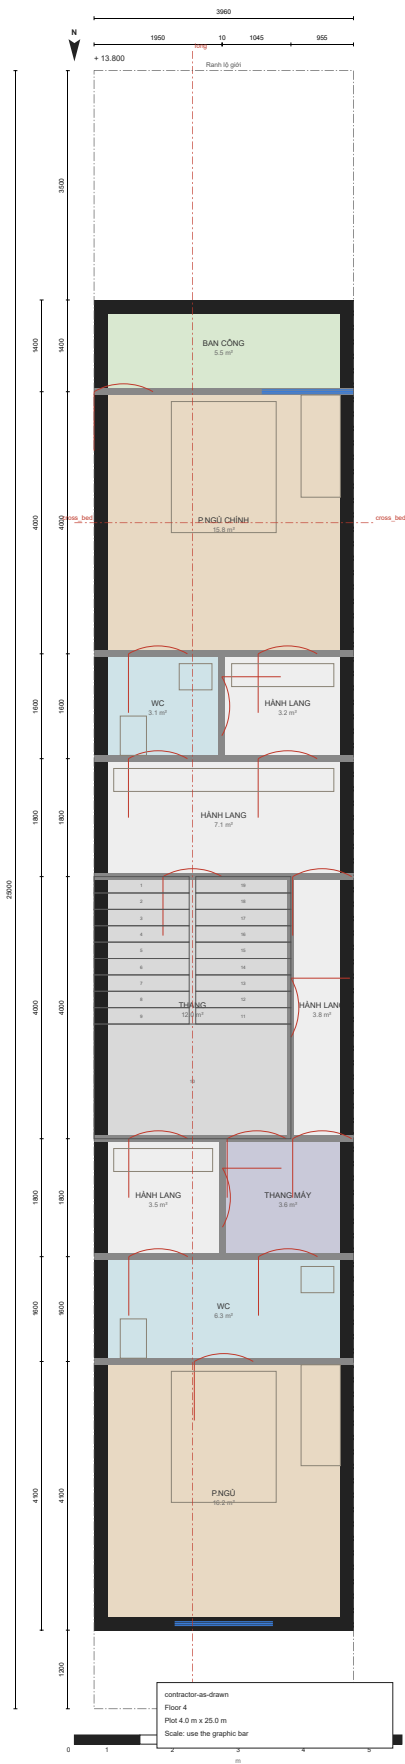


Floor 5 — Floor Plan

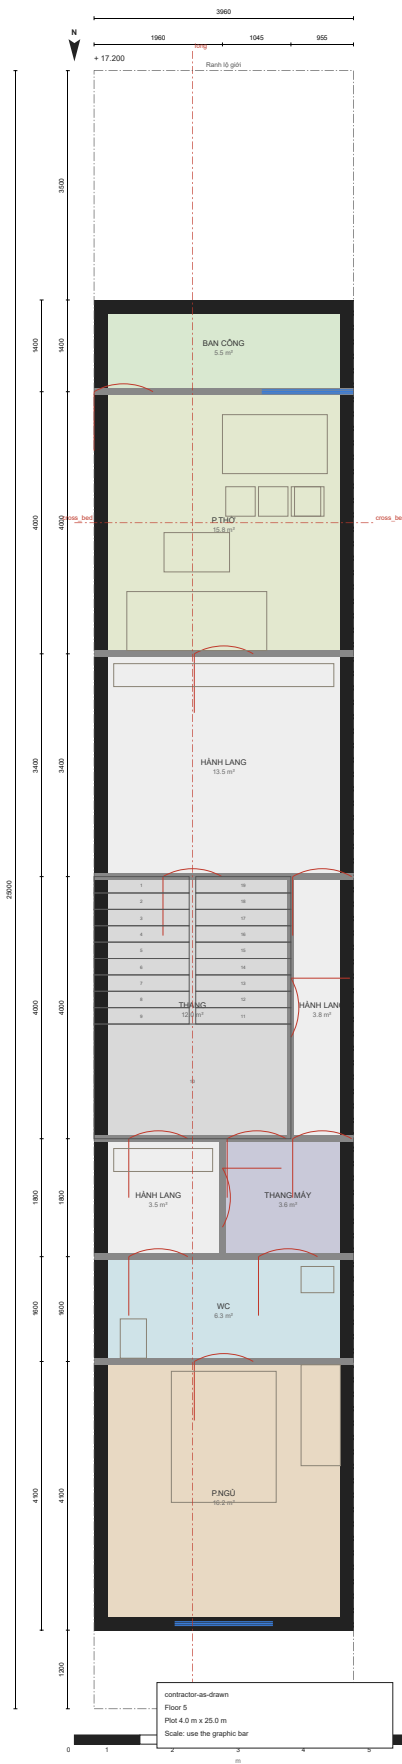


Roof Terrace — Floor Plan

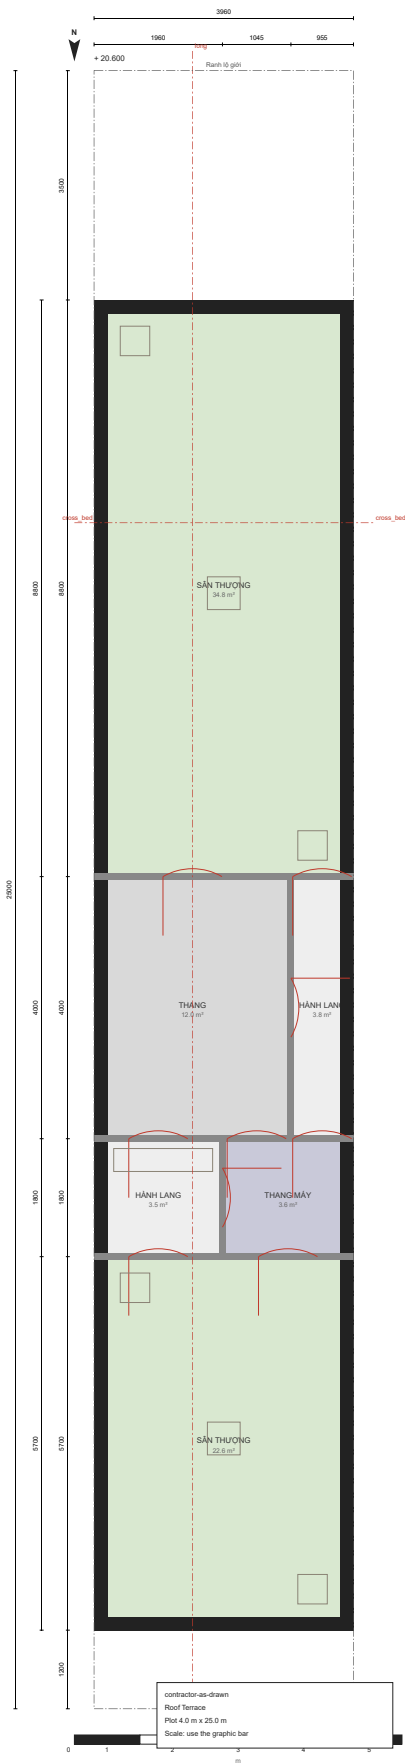


North Elevation

 


South Elevation

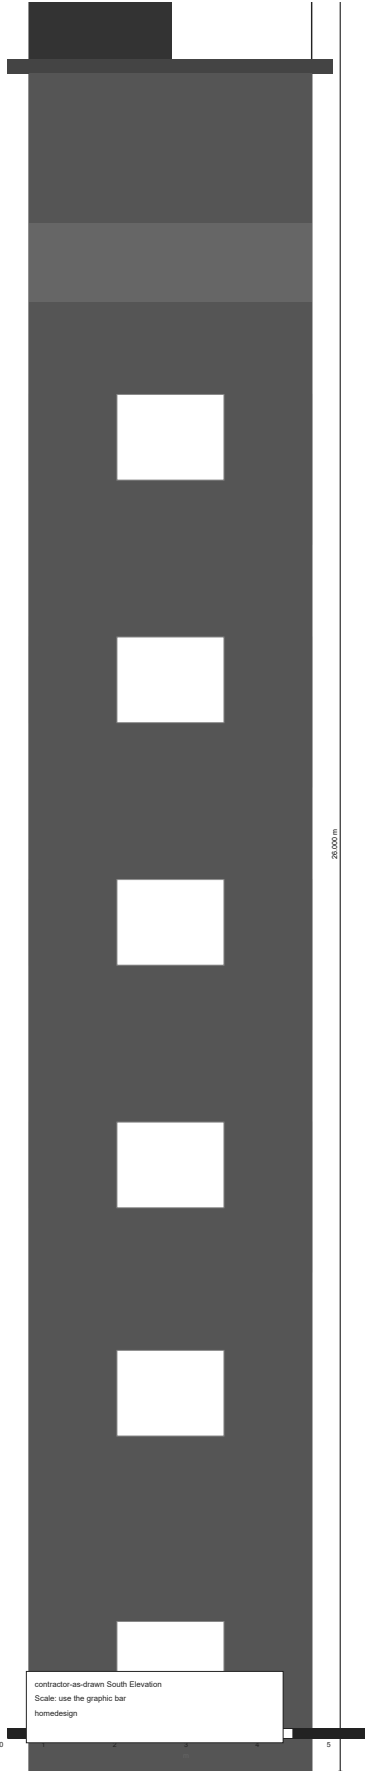


East Elevation

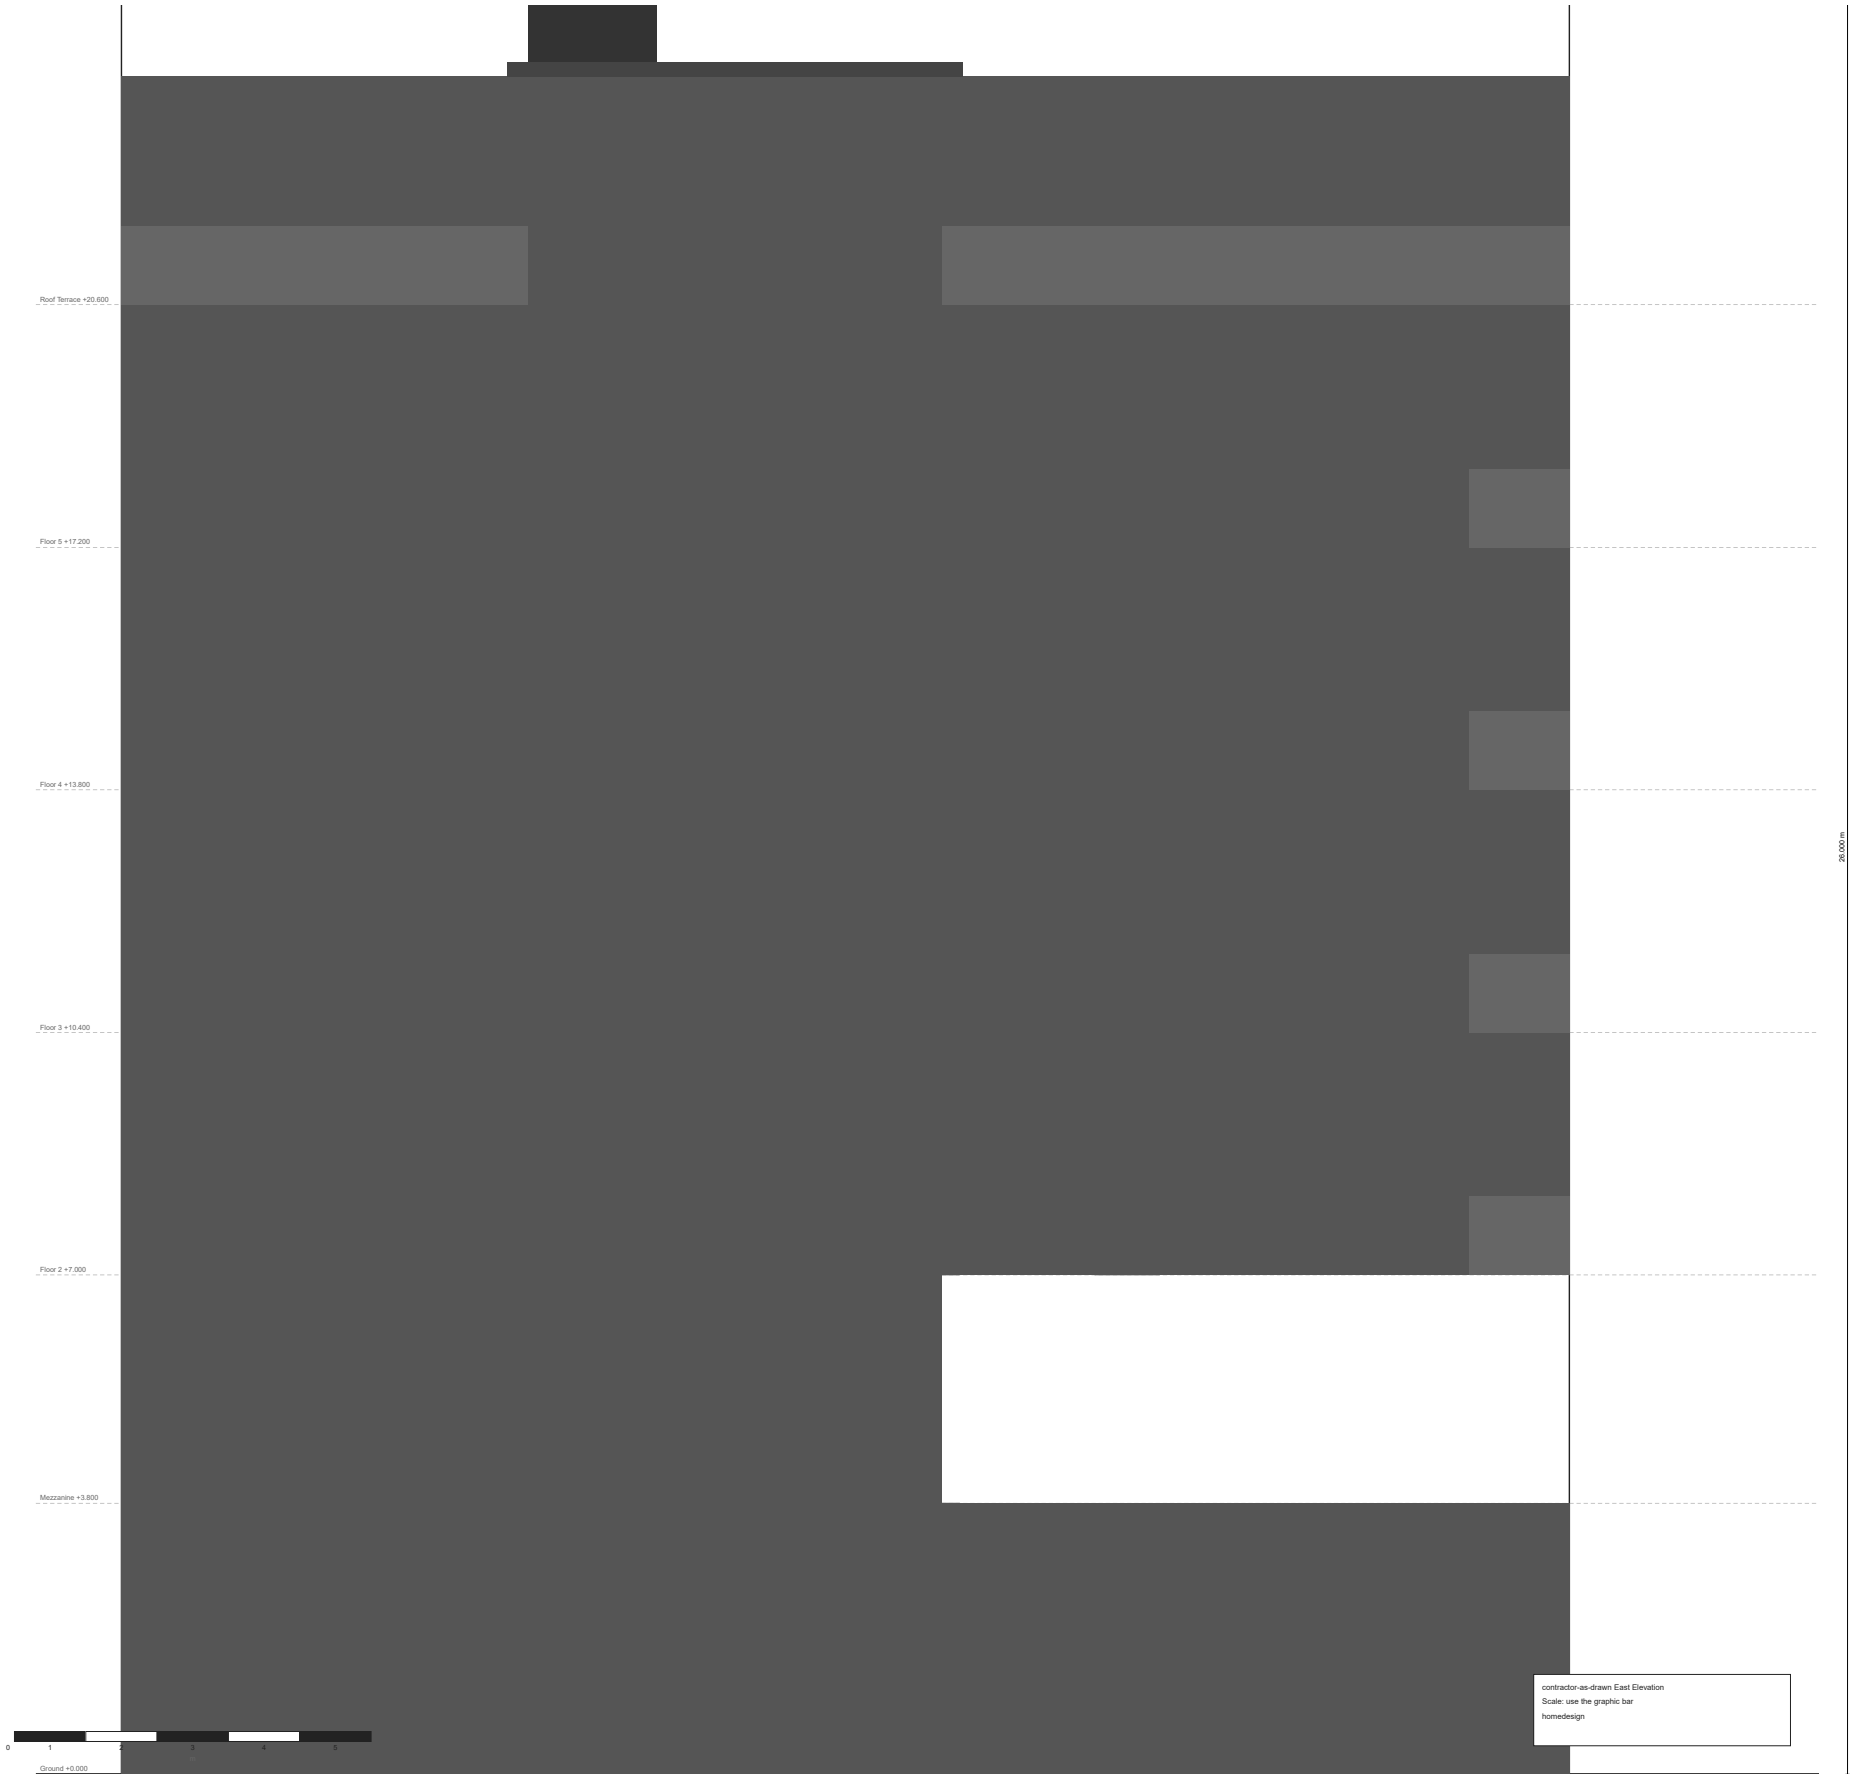


West Elevation

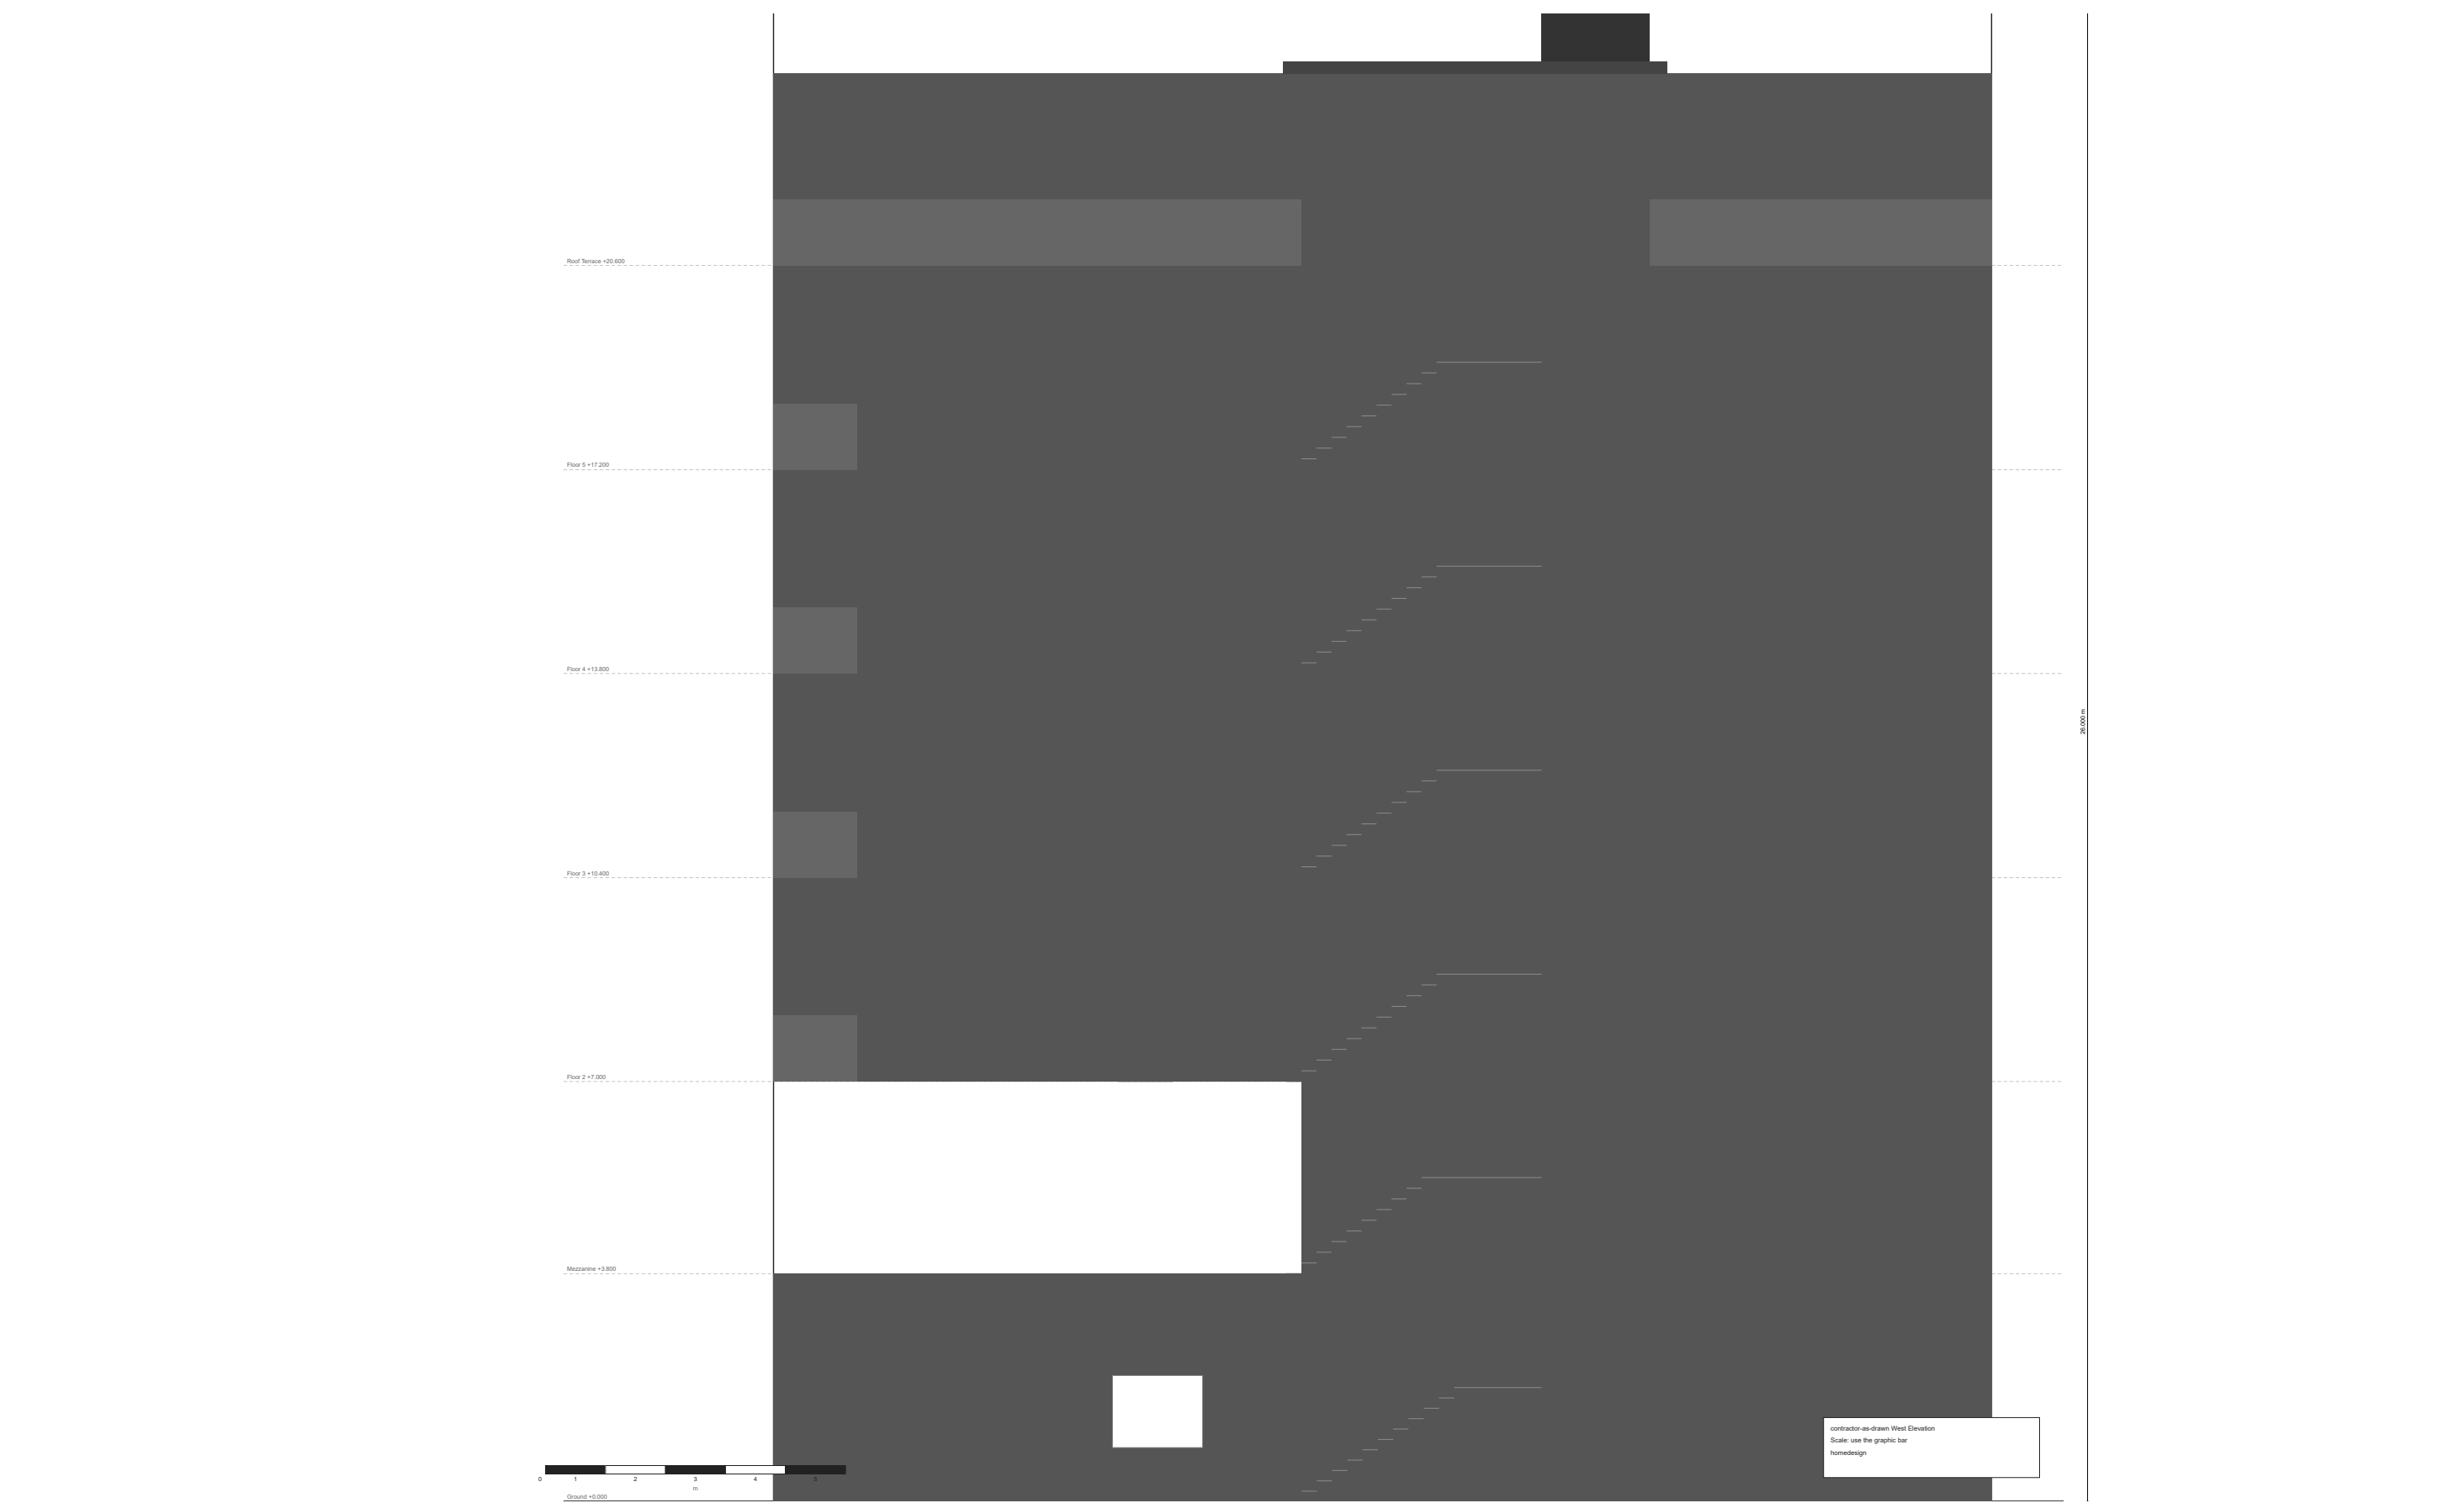



long — Long Section

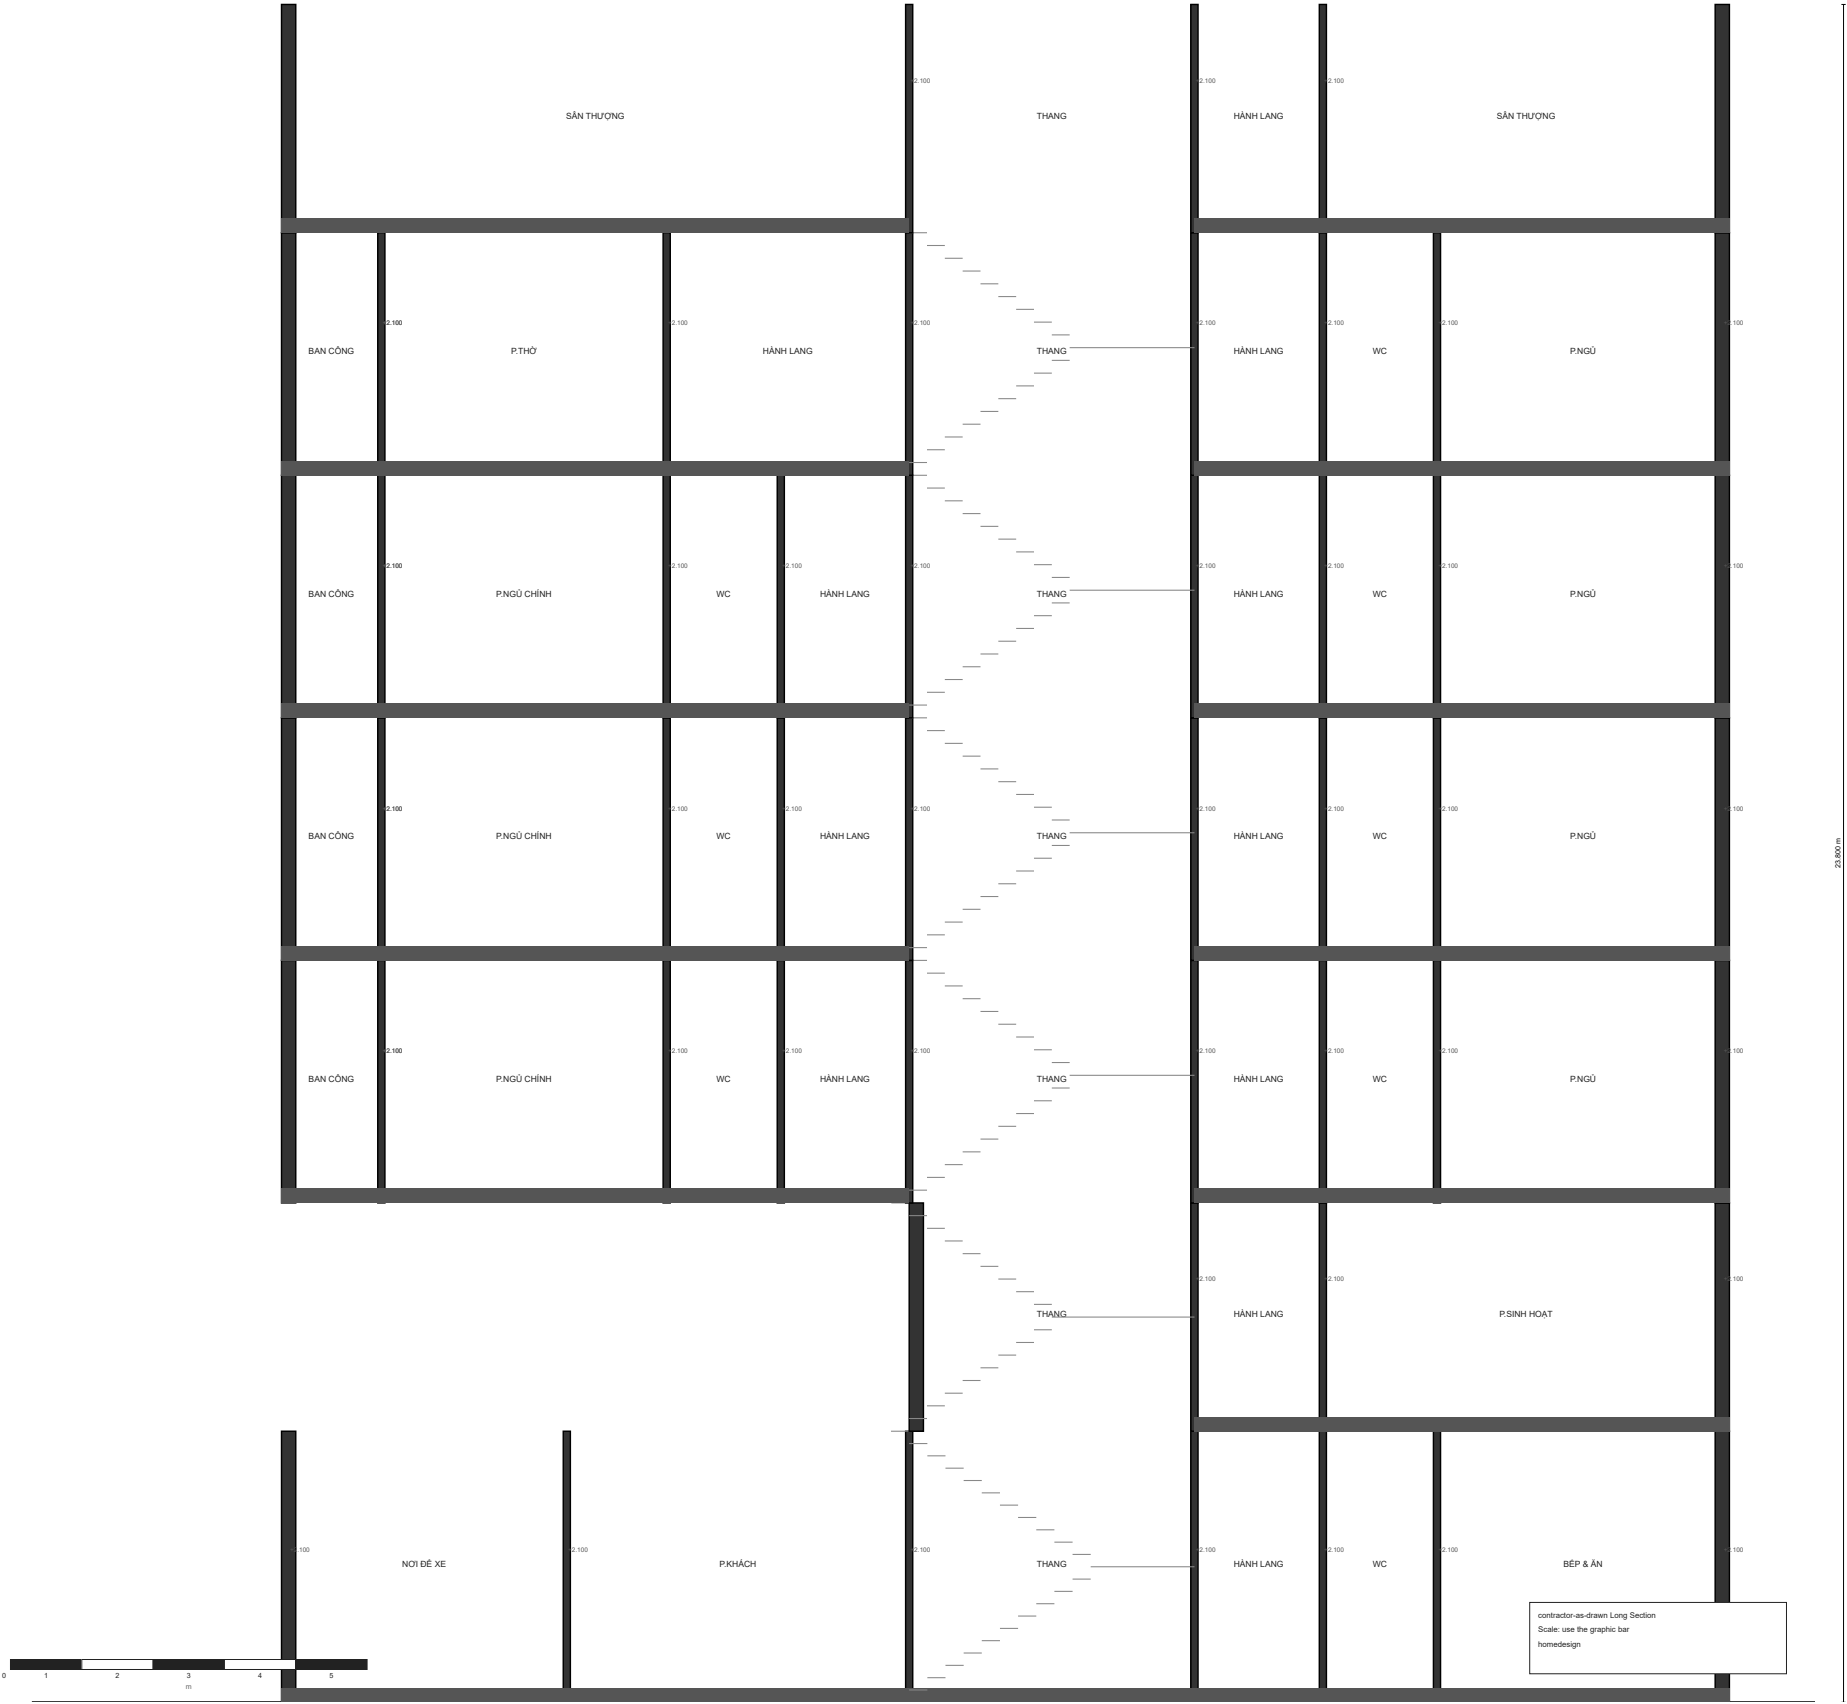


cross_bed — Cross Section

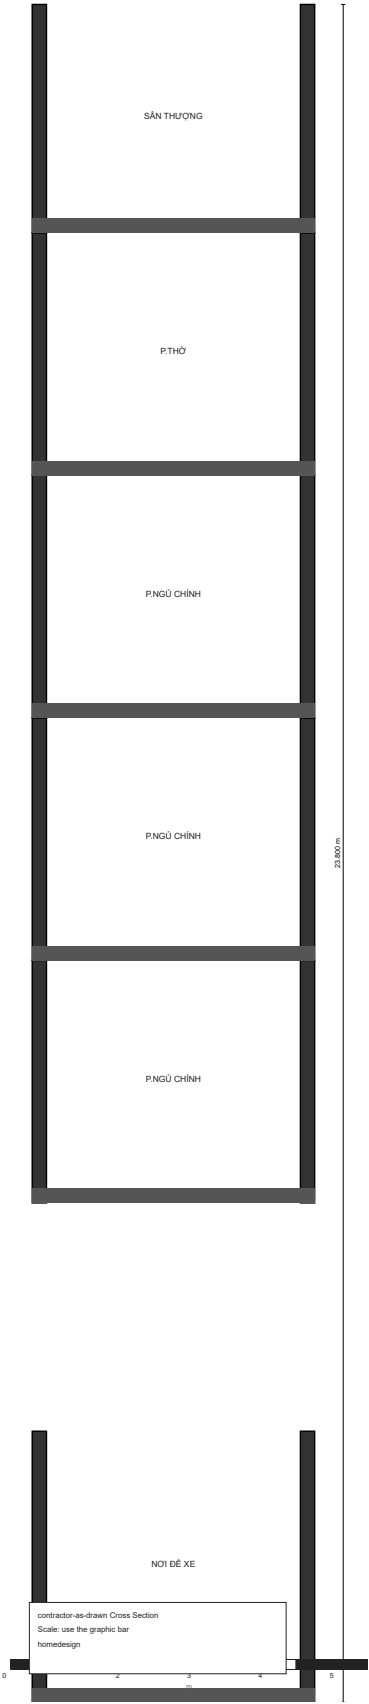


Renders

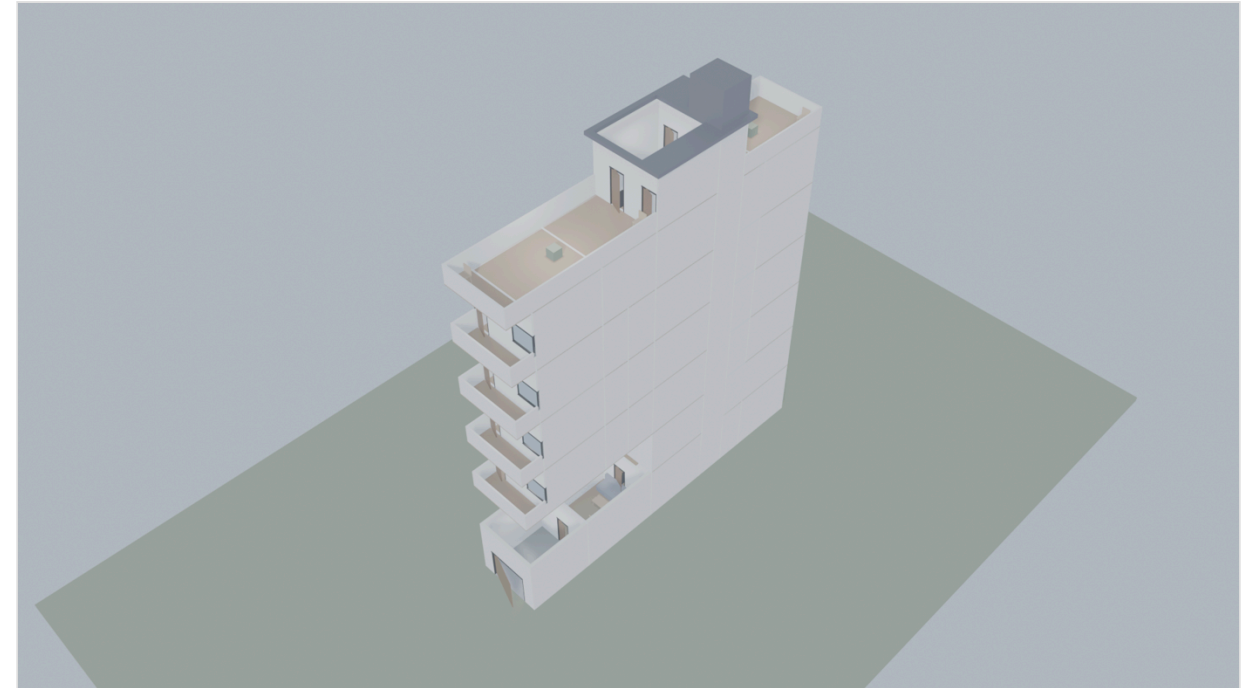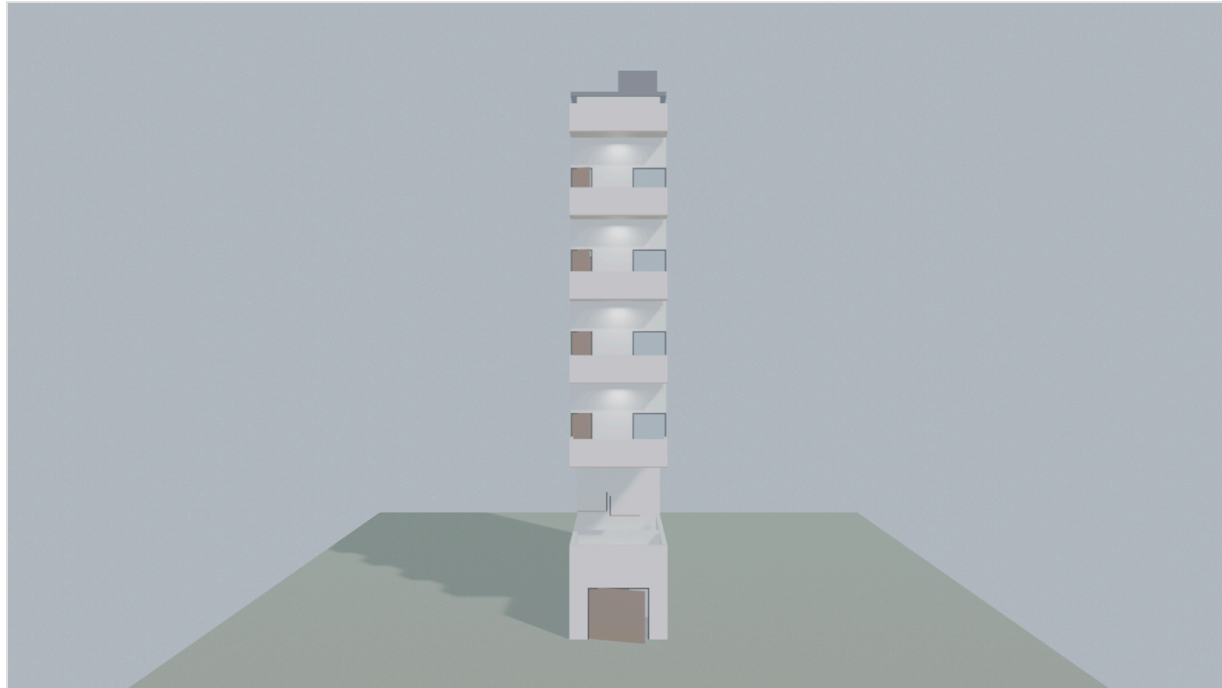


Renders

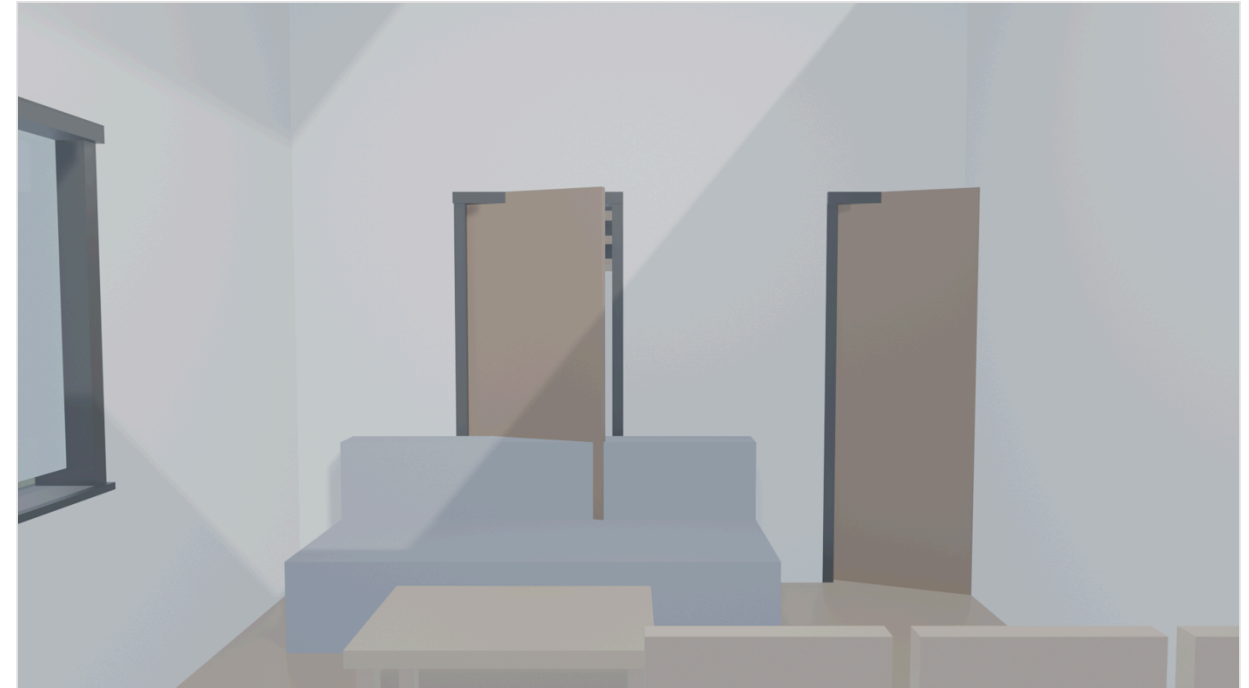



Renders

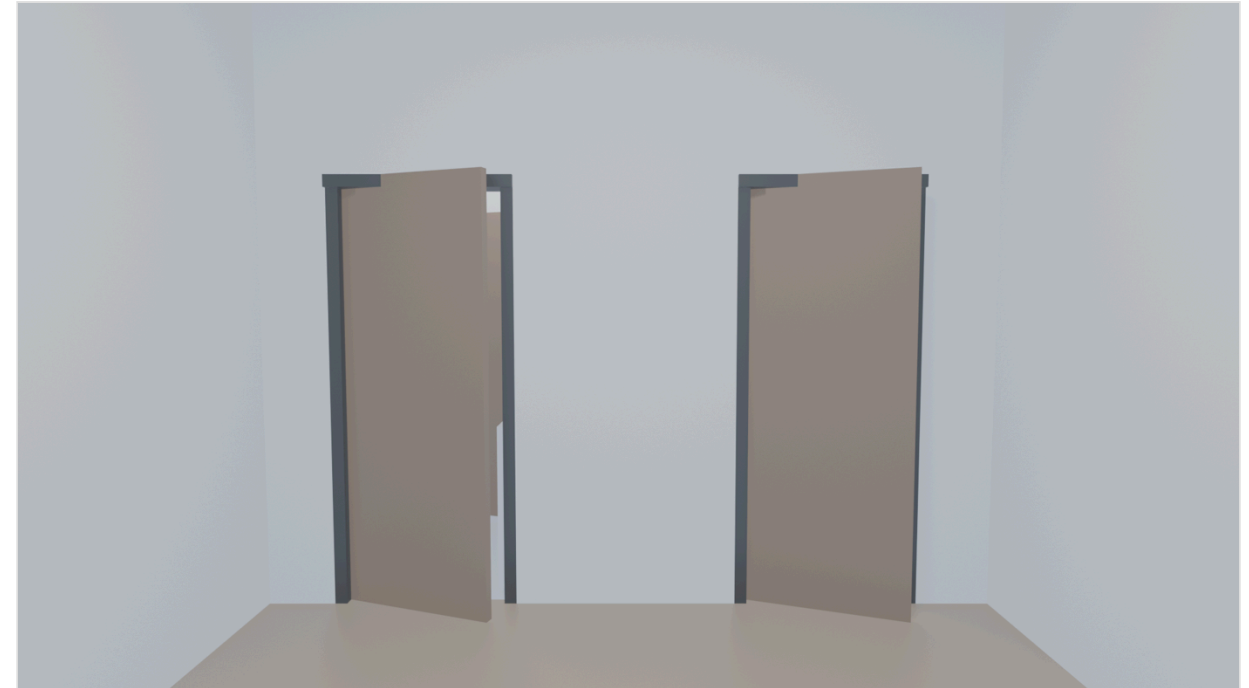

Renders

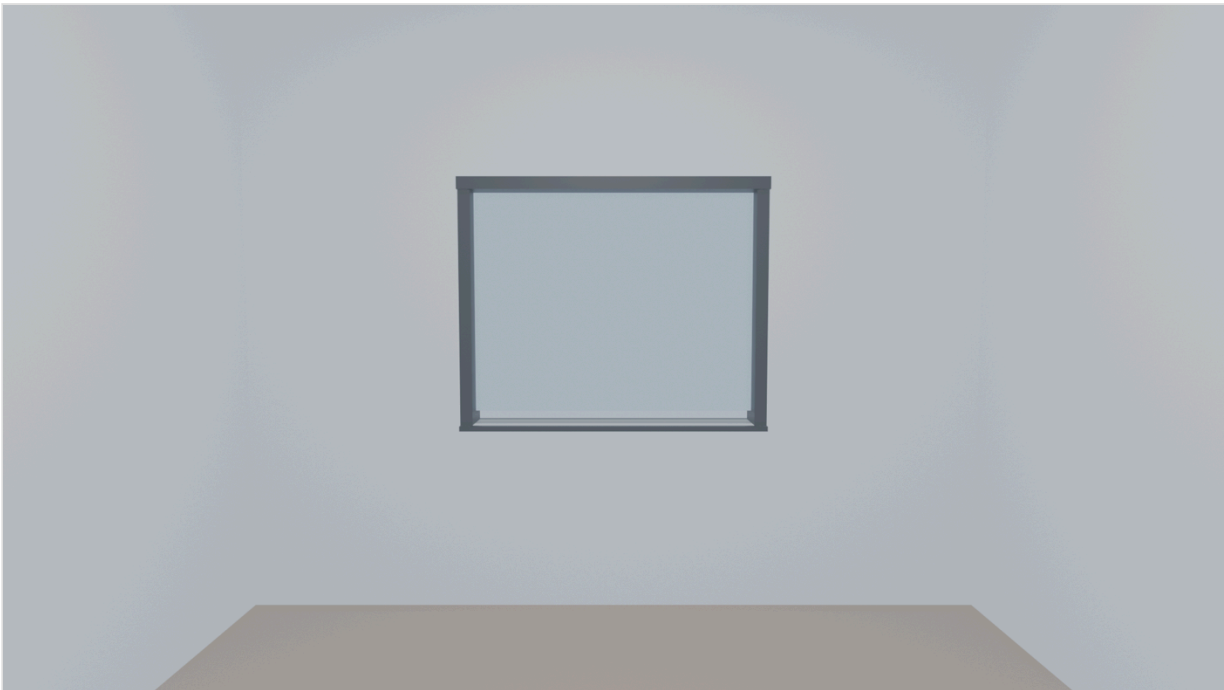

Renders

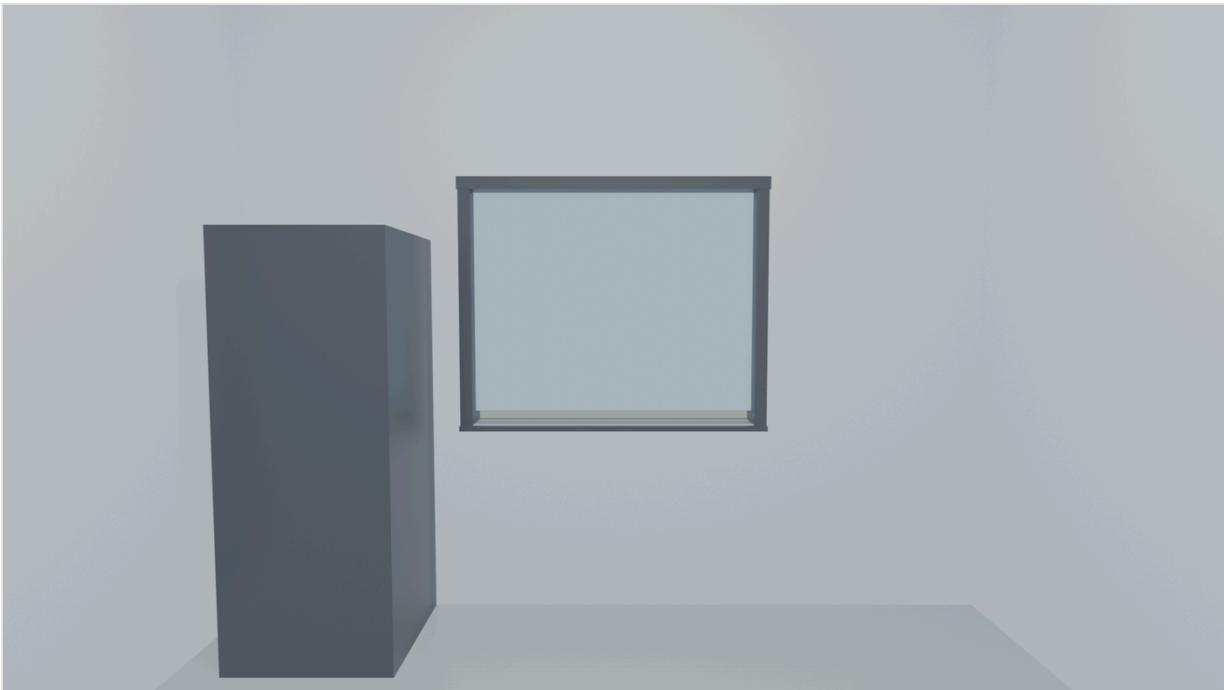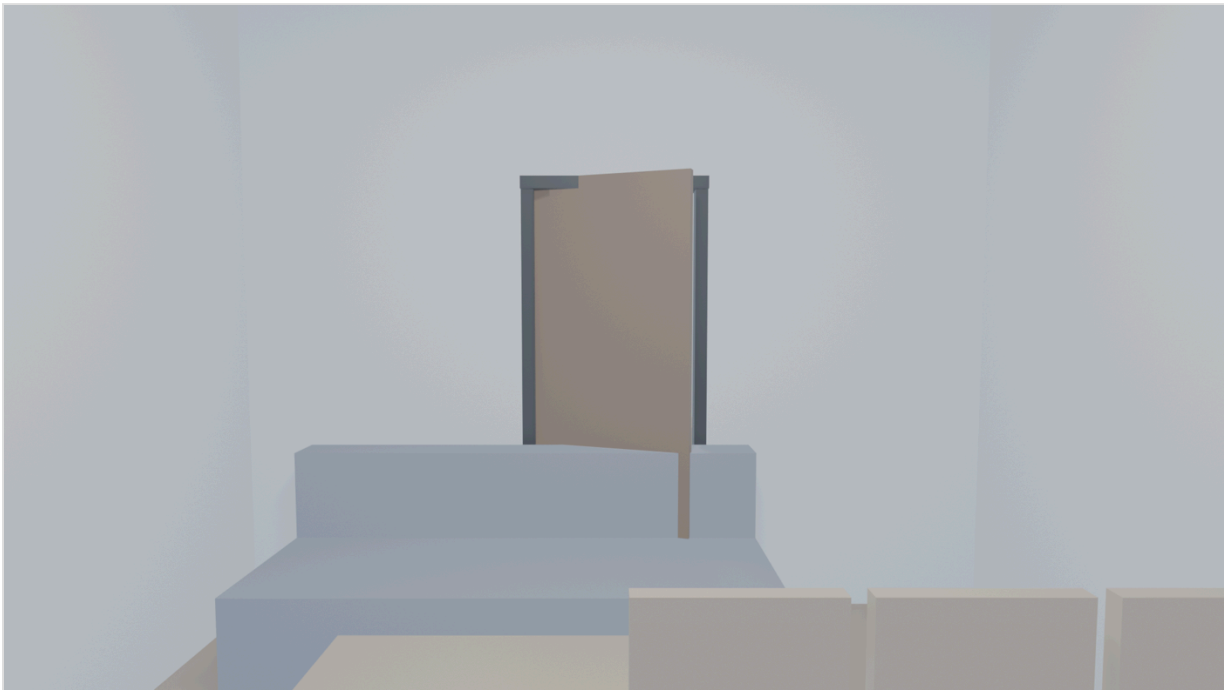

Renders



Requirements for the Architect

- Confirm the inferred lift shaft (2,000 × 1,800 mm, byte-identical on all levels) against the unlabelled walled void on the drawing.
- Confirm the enlarged stair shaft (3,005 × 4,000 mm) — the drawn 3,005 × 3,200 shaft cannot hold a U-return at the 3,800 mm storey height.
- Confirm the reconstructed programme room-by-room against the sheets (see designs/contractor-as-drawn.measurements.md).

Door & Window Schedule

ID	Floor	Type	Width	Sill	Head	Between
F0_O000	0	door	900	0	2100	exterior / ?
F0_O001	0	door	900	0	2100	exterior / ?
F0_O002	0	door	900	0	2100	exterior / ?
F0_O003	0	door	900	0	2100	exterior / ?
F0_O004	0	door	900	0	2100	exterior / ?
F0_O005	0	door	900	0	2100	exterior / ?
F0_O006	0	door	900	0	2100	exterior / ?
F0_O007	0	door	900	0	2100	exterior / ?
F0_O008	0	door	900	0	2100	exterior / ?
F0_O009	0	door	900	0	2100	exterior / ?
F0_O010	0	door	900	0	2100	exterior / ?
F0_O011	0	door	2500	0	2100	exterior / ?
F0_O012	0	window	1500	900	2100	exterior / ?
F0_O013	0	window	1500	900	2100	exterior / ?
F1_O000	1	door	900	0	2100	exterior / ?
F1_O001	1	door	900	0	2100	exterior / ?
F1_O002	1	door	900	0	2100	exterior / ?
F1_O003	1	door	900	0	2100	exterior / ?
F1_O004	1	door	900	0	2100	exterior / ?
F1_O005	1	door	900	0	2100	exterior / ?
F1_O006	1	door	900	0	2100	exterior / ?
F1_O007	1	window	1500	900	2100	exterior / ?
F2_O000	2	door	900	0	2100	exterior / ?
F2_O001	2	window	1400	900	2100	exterior / ?
F2_O002	2	door	900	0	2100	exterior / ?
F2_O003	2	door	900	0	2100	exterior / ?
F2_O004	2	door	900	0	2100	exterior / ?
F2_O005	2	door	900	0	2100	exterior / ?
F2_O006	2	door	900	0	2100	exterior / ?
F2_O007	2	door	900	0	2100	exterior / ?
F2_O008	2	door	900	0	2100	exterior / ?
F2_O009	2	door	900	0	2100	exterior / ?
F2_O010	2	door	900	0	2100	exterior / ?
F2_O011	2	door	900	0	2100	exterior / ?
F2_O012	2	door	900	0	2100	exterior / ?
F2_O013	2	door	900	0	2100	exterior / ?
F2_O014	2	door	900	0	2100	exterior / ?
F2_O015	2	door	900	0	2100	exterior / ?
F2_O016	2	door	900	0	2100	exterior / ?
F2_O017	2	window	1500	900	2100	exterior / ?
F3_O000	3	door	900	0	2100	exterior / ?
F3_O001	3	window	1400	900	2100	exterior / ?

ID	Floor	Type	Width	Sill	Head	Between
F3_O010	3	door	900	0	2100	exterior / ?
F3_O011	3	door	900	0	2100	exterior / ?
F3_O012	3	door	900	0	2100	exterior / ?
F3_O013	3	door	900	0	2100	exterior / ?
F3_O014	3	door	900	0	2100	exterior / ?
F3_O015	3	door	900	0	2100	exterior / ?
F3_O016	3	door	900	0	2100	exterior / ?
F3_O017	3	window	1500	900	2100	exterior / ?
F4_O000	4	door	900	0	2100	exterior / ?
F4_O001	4	window	1400	900	2100	exterior / ?
F4_O002	4	door	900	0	2100	exterior / ?
F4_O003	4	door	900	0	2100	exterior / ?
F4_O004	4	door	900	0	2100	exterior / ?
F4_O005	4	door	900	0	2100	exterior / ?
F4_O006	4	door	900	0	2100	exterior / ?
F4_O007	4	door	900	0	2100	exterior / ?
F4_O008	4	door	900	0	2100	exterior / ?
F4_O009	4	door	900	0	2100	exterior / ?
F4_O010	4	door	900	0	2100	exterior / ?
F4_O011	4	door	900	0	2100	exterior / ?
F4_O012	4	door	900	0	2100	exterior / ?
F4_O013	4	door	900	0	2100	exterior / ?
F4_O014	4	door	900	0	2100	exterior / ?
F4_O015	4	door	900	0	2100	exterior / ?
F4_O016	4	door	900	0	2100	exterior / ?
F4_O017	4	window	1500	900	2100	exterior / ?
F5_O000	5	door	900	0	2100	exterior / ?
F5_O001	5	window	1400	900	2100	exterior / ?
F5_O002	5	door	900	0	2100	exterior / ?
F5_O003	5	door	900	0	2100	exterior / ?
F5_O004	5	door	900	0	2100	exterior / ?
F5_O005	5	door	900	0	2100	exterior / ?
F5_O006	5	door	900	0	2100	exterior / ?
F5_O007	5	door	900	0	2100	exterior / ?
F5_O008	5	door	900	0	2100	exterior / ?
F5_O009	5	door	900	0	2100	exterior / ?
F5_O010	5	door	900	0	2100	exterior / ?
F5_O011	5	door	900	0	2100	exterior / ?
F5_O012	5	door	900	0	2100	exterior / ?
F5_O013	5	window	1500	900	2100	exterior / ?
F6_O000	6	door	900	0	2100	exterior / ?
F6_O001	6	door	900	0	2100	exterior / ?

Quantity Take-Off

Storey	GFA (m²)	Ext. wall (m)	Partition wall (m)	Doors	Windows
Ground	80.4	41.0	6.7	12	2
Mezzanine	45.5	23.6	6.3	7	1
Floor 2	80.4	41.0	8.7	16	2
Floor 3	80.4	41.0	8.7	16	2
Floor 4	80.4	41.0	8.7	16	2
Floor 5	80.4	41.0	6.8	12	2
Roof Terrace	80.4	41.0	6.5	9	0
Built envelope (W x D m)	4.0	20.3	0.0		
Total	527.9	269.6	52.4	88	11

Handover Files

The following machine-readable files accompany this brief:

- contractor-as-drawn.json (source spec, JSON)
- contractor-as-drawn_f0.dxf (Ground, CAD/DXF)
- contractor-as-drawn_f1.dxf (Mezzanine, CAD/DXF)
- contractor-as-drawn_f2.dxf (Floor 2, CAD/DXF)
- contractor-as-drawn_f3.dxf (Floor 3, CAD/DXF)
- contractor-as-drawn_f4.dxf (Floor 4, CAD/DXF)
- contractor-as-drawn_f5.dxf (Floor 5, CAD/DXF)
- contractor-as-drawn_f6.dxf (Roof Terrace, CAD/DXF)